
MẶT BẰNG TỔNG THỂ CỤM CÔNG TRÌNH ĐẦU MỐI HỒ CÀ GIÂY

TỶ LỆ: 1/2000

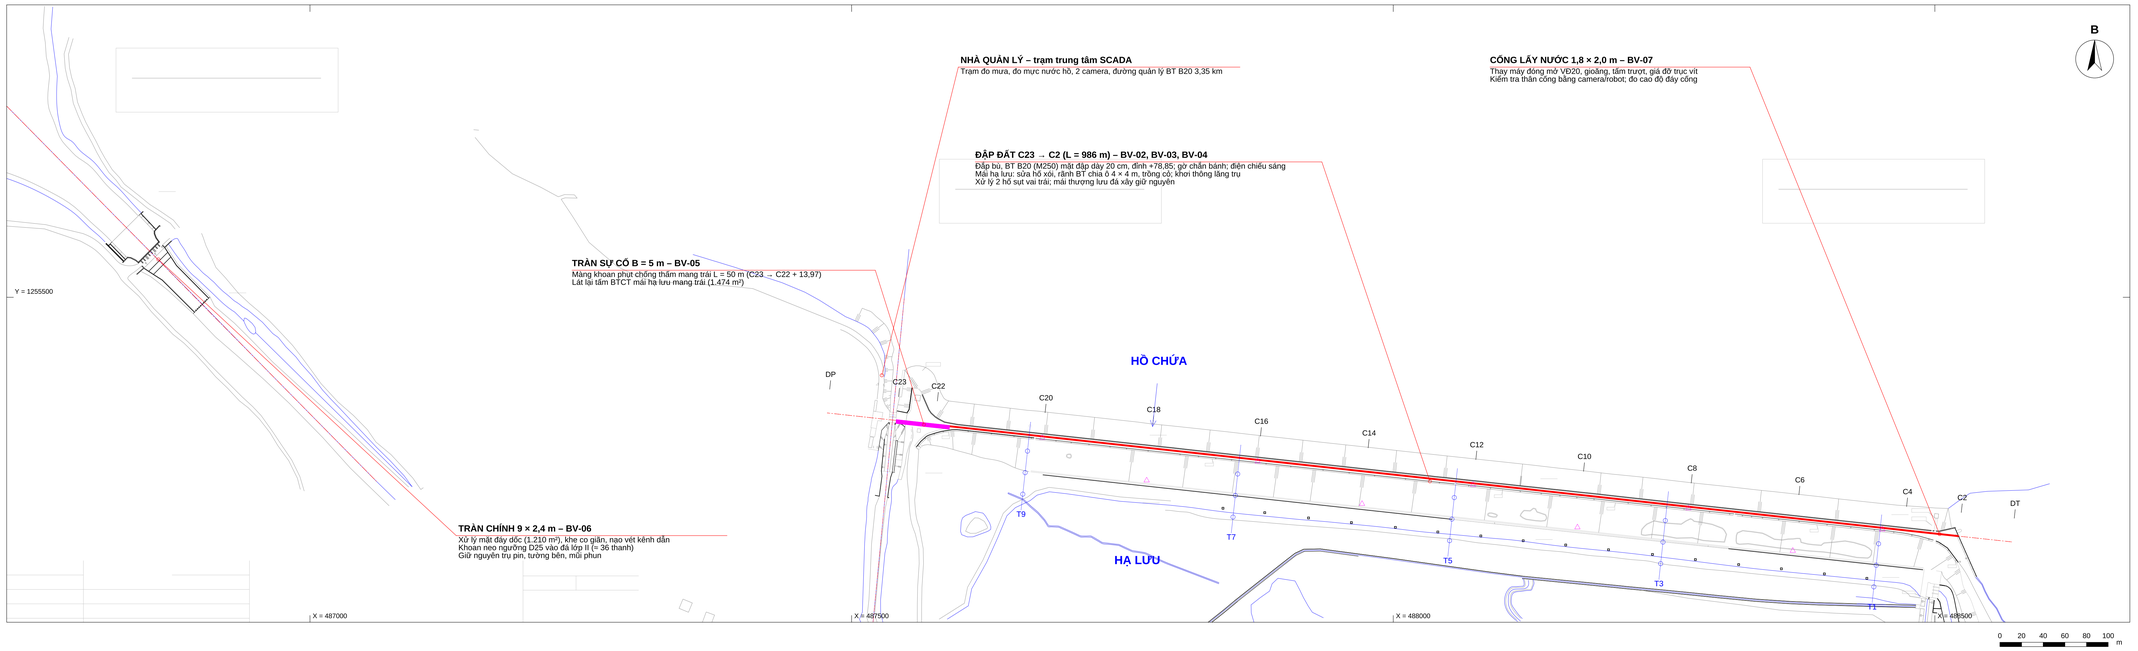

TỔNG HỢP GIẢI PHÁP SỬA CHỮA, NÂNG CẤP

Hạng mục	Giải pháp sửa chữa, nâng cấp được chọn (Bảng 3.2)
Đập đất	Đắp bù, gia cố mặt đập BT B20 (M250) dày 20 cm, đỉnh +78,85 m; gờ chắn bánh; điện chiếu sáng; sửa hố xói, hệ rãnh BT, trồng cỏ mái hạ lưu; xử lý hố sụt vai trái; khơi thông lăng trụ
Tràn chính	Giữ nguyên quy mô; sửa chữa bề mặt dây dốc, khe co giãn; nạo vét kênh dẫn; khoan neo ngưỡng D25
Tràn sự cố	Màng khoan phụt XM – sét mang trái (L = 50 m, 3 hàng TKCS; đề xuất 3 hàng 15 m + 2 hàng A, B); lát lại tấm BT mái
Cống lấy nước	Thay 2 máy đóng mở VĐ20; thay gioăng, tấm trượt; bổ sung giá đỡ trục vít; kiểm tra thân cống, đo cao độ đáy cống
Quan trắc, SCADA	14 giếng quan trắc thấm tự động (T1, T3, T5, T7, T9), 9 mốc lún, trạm đo mưa, đo mực nước, camera, trạm trung tâm
Đường quản lý	Bê tông hóa 3,35 km, mặt BT B20 (M250) rộng 4 m

KÝ HIỆU

- Đập đất sửa chữa, nâng cấp (tim đập C23 → C2)
- Tim tuyến công trình
- Màng khoan phụt chống thấm mang trái tràn sự cố
- Tường, kết cấu BT hiện trạng
- Mái đập, mái đào (nền bình đồ TKCS)
- Tuyến quan trắc thấm, giếng tự động
- Mốc quan trắc lún
- Địa vật, đường (nền bình đồ TKCS)


GHI CHÚ:
1. Hệ tọa độ VN-2000, cao độ Quốc gia; kích thước, cao trình ghi bằng m. Nền bình đồ trích từ hồ sơ TKCS (tỷ lệ gốc 1/1000), thể hiện lại ở tỷ lệ 1/2000.
2. Lý trình theo tim đập từ cọc DP; đập đất từ C23 (tường bên trái tràn sự cố, lý trình 63,98) đến C2 (1050,73), dài 986 m. Cao trình đỉnh đập sau sửa chữa +78,85 (mép thượng lưu), TKCS +78,75.
3. Vị trí tuyến quan trắc T1 ÷ T9 theo hồ sơ hiện trạng; vị trí mốc lún mới thể hiện sơ đồ, chuẩn xác khi lập bản vẽ thi công.
4. Chi tiết các hạng mục xem: BV-02 cắt dọc đập; BV-03, BV-04 đập đất; BV-05 khoan phụt (chuyển đề); BV-06 tràn chính; BV-07 cống lấy nước.

THÔNG SỐ CHỦ YẾU

Thông số	Đơn vị	Giá trị
Cấp công trình	--	II
MNDBT / MNC	m	+74,70 / +67,50
MNLTK (P = 1%) / MNLKT (P = 0,2%)	m	+77,63 / +78,54
Dung tích ứng với MNDBT (tính lại)	10^6 m³	36,41
Đỉnh đập hiện trạng / TKCS / đề án	m	+78,35 / +78,75 / +78,85
Đỉnh tường chắn sóng (giữ nguyên)	m	+79,40
Chiều dài / bề rộng đỉnh đập	m	986 / 5,0
Tràn chính: ngưỡng, b	m	+74,70; 9 × 2,4
Tràn sự cố: ngưỡng, b	m	+71,00; 5,0
Cống: ngưỡng, b × h, L	m	+65,60; 1,8 × 2,0; 67


HÌNH TRÍCH A – KHU VỰC TRÀN SỰ CỐ, NHÀ QUẢN LÝ, ĐẦU ĐẬP TRÁI

TỶ LỆ: 1/1000

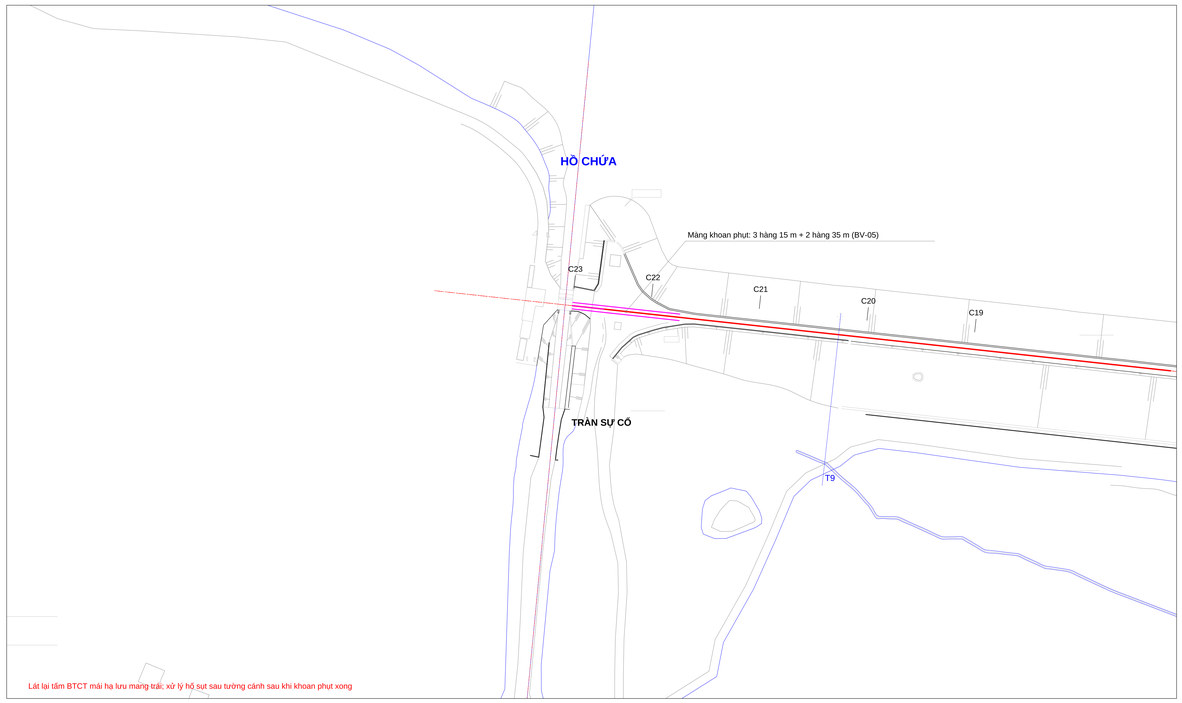

HÌNH TRÍCH B – KHU VỰC CỐNG LẤY NƯỚC, VAI PHẢI

TỶ LỆ: 1/1000

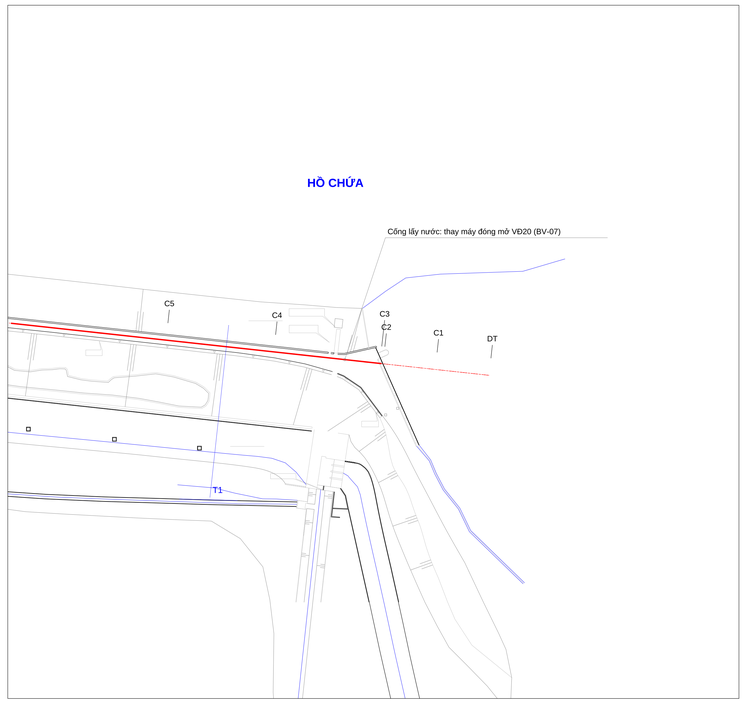

TRƯỜNG ĐẠI HỌC THỦY LỢI – PHÂN HIỆU TẠI TP. HỒ CHÍ MINH				
KHOA CÔNG TRÌNH – ĐỒ ÁN TỐT NGHIỆP KỸ SƯ				
ĐỀ TÀI: TÍNH TOÁN, THIẾT KẾ SỬA CHỮA NÂNG CẤP CỤM CÔNG TRÌNH ĐẦU MỐI HỒ CHỨA NƯỚC CÀ GIÂY – TỈNH LÂM ĐỒNG				
MẶT BẰNG TỔNG THỂ CỤM ĐẦU MỐI BỐ TRÍ CÁC HẠNG MỤC SỬA CHỮA, NÂNG CẤP				
GV HƯỚNG DẪN	TS. Phạm Ngọc Thịnh		TỶ LỆ	**1/2000**
SV THỰC HIỆN	Trần Quốc Thanh		BẢN VẼ SỐ	**01 / 07**
NGÀNH	KTXD công trình thủy	Tháng 10/2026	KÝ HIỆU	**HCG-BV01**